


E30 Unterstation

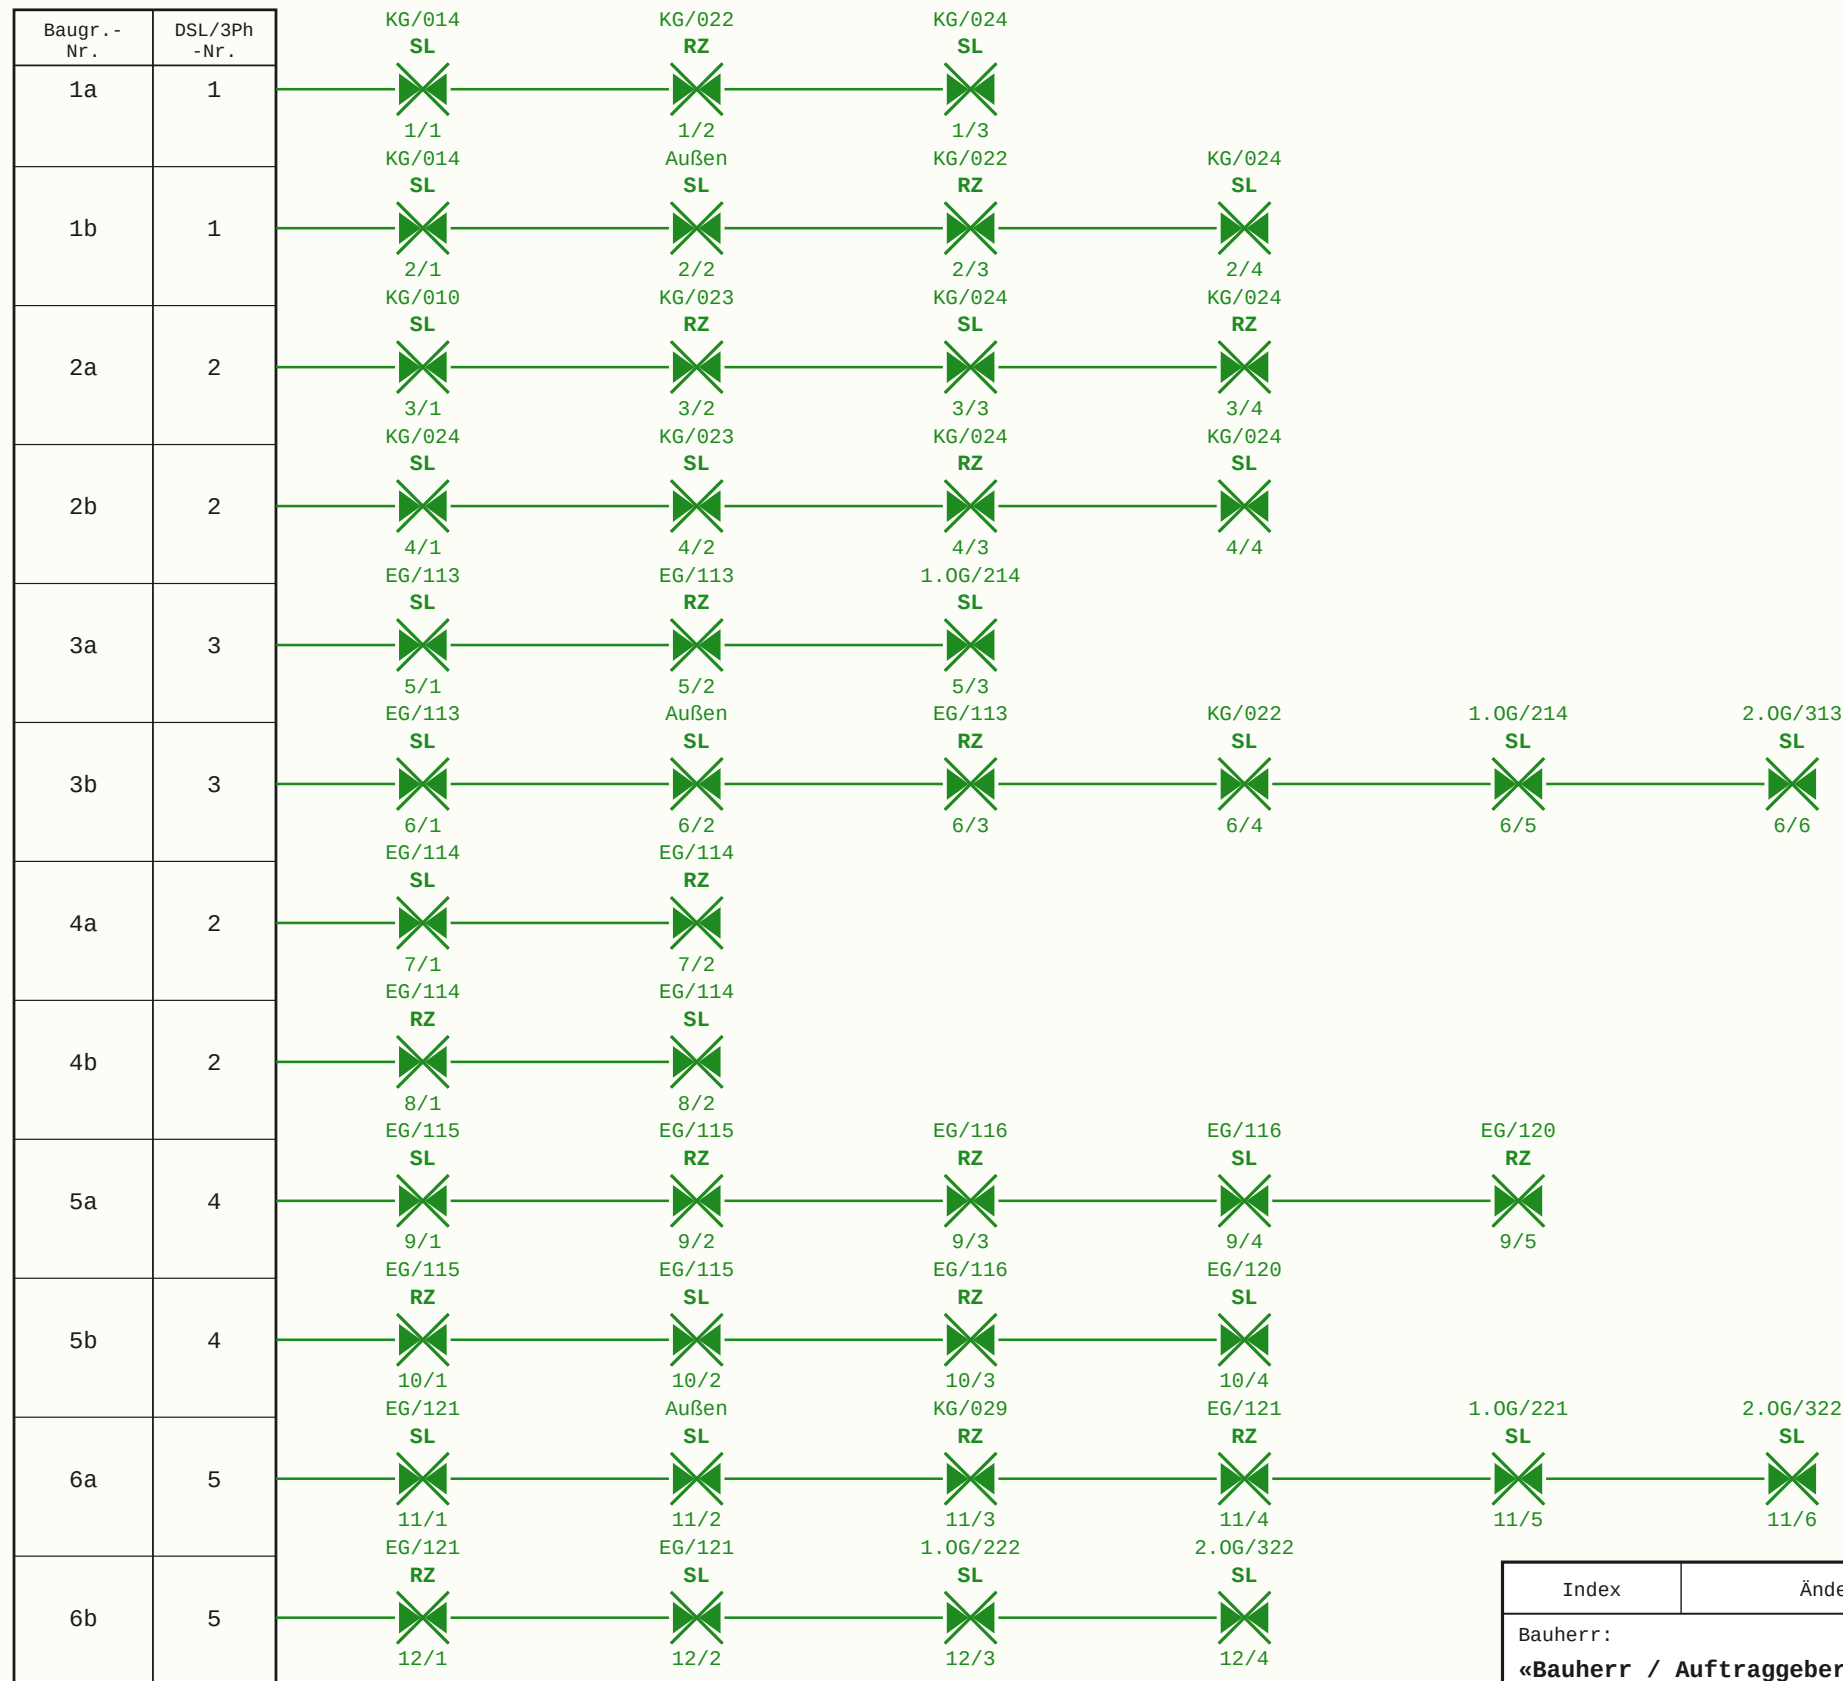

weitere Stromkreise 13/1 ... 20/5 (1. OG / 2. OG) analog

Einspeisung 5 x 25 qmm von Zentralbatterie
Einbau von externen DLS/3Ph-Bus-Modul in folgende Verteilungen:
UV 1.1, 1.2 / UV 2.1, 2.2 / UV 3.1, 3.2
Verdrahtung der Bus-Module mit IY(ST)Y 2x2x0,8

B Bereitschaftslicht
D Dauerlicht
DL geschaltetes Dauerlicht

Alle RZ-Leuchten in Dauerlicht

Alle nicht gekennzeichneten
Sicherheitsleuchten in
geschaltetem Dauerlicht
über EIB in Verbindung
mit DLS-Modul.

Index	Änderung	Name	Datum	
Bauherr: «Bauherr / Auftraggeber»				«Elektrofirma» Meisterbetrieb «Straße · PLZ Ort · Tel.»
Objekt: «Bauvorhaben, Straße, Ort»				
Darstellung: Übersichtsplan Elektrotechnik Sicherheitsbeleuchtung – E30-Unterstation			Projekt-Id.-Nr.: «0000-00.0» Maßstab: o. M. Bl.-Nr.: 006A	
Zeichnungs-Nr.: «731.00 – 01 – A – EL – 8 – 006A / 03»			Planer/Datum: «Name» / 05.07.2026	